


Andar 2
1 : 50

Área Construída (Terreno)
147 m²

Área a ser Construída (2)
99.32 m²

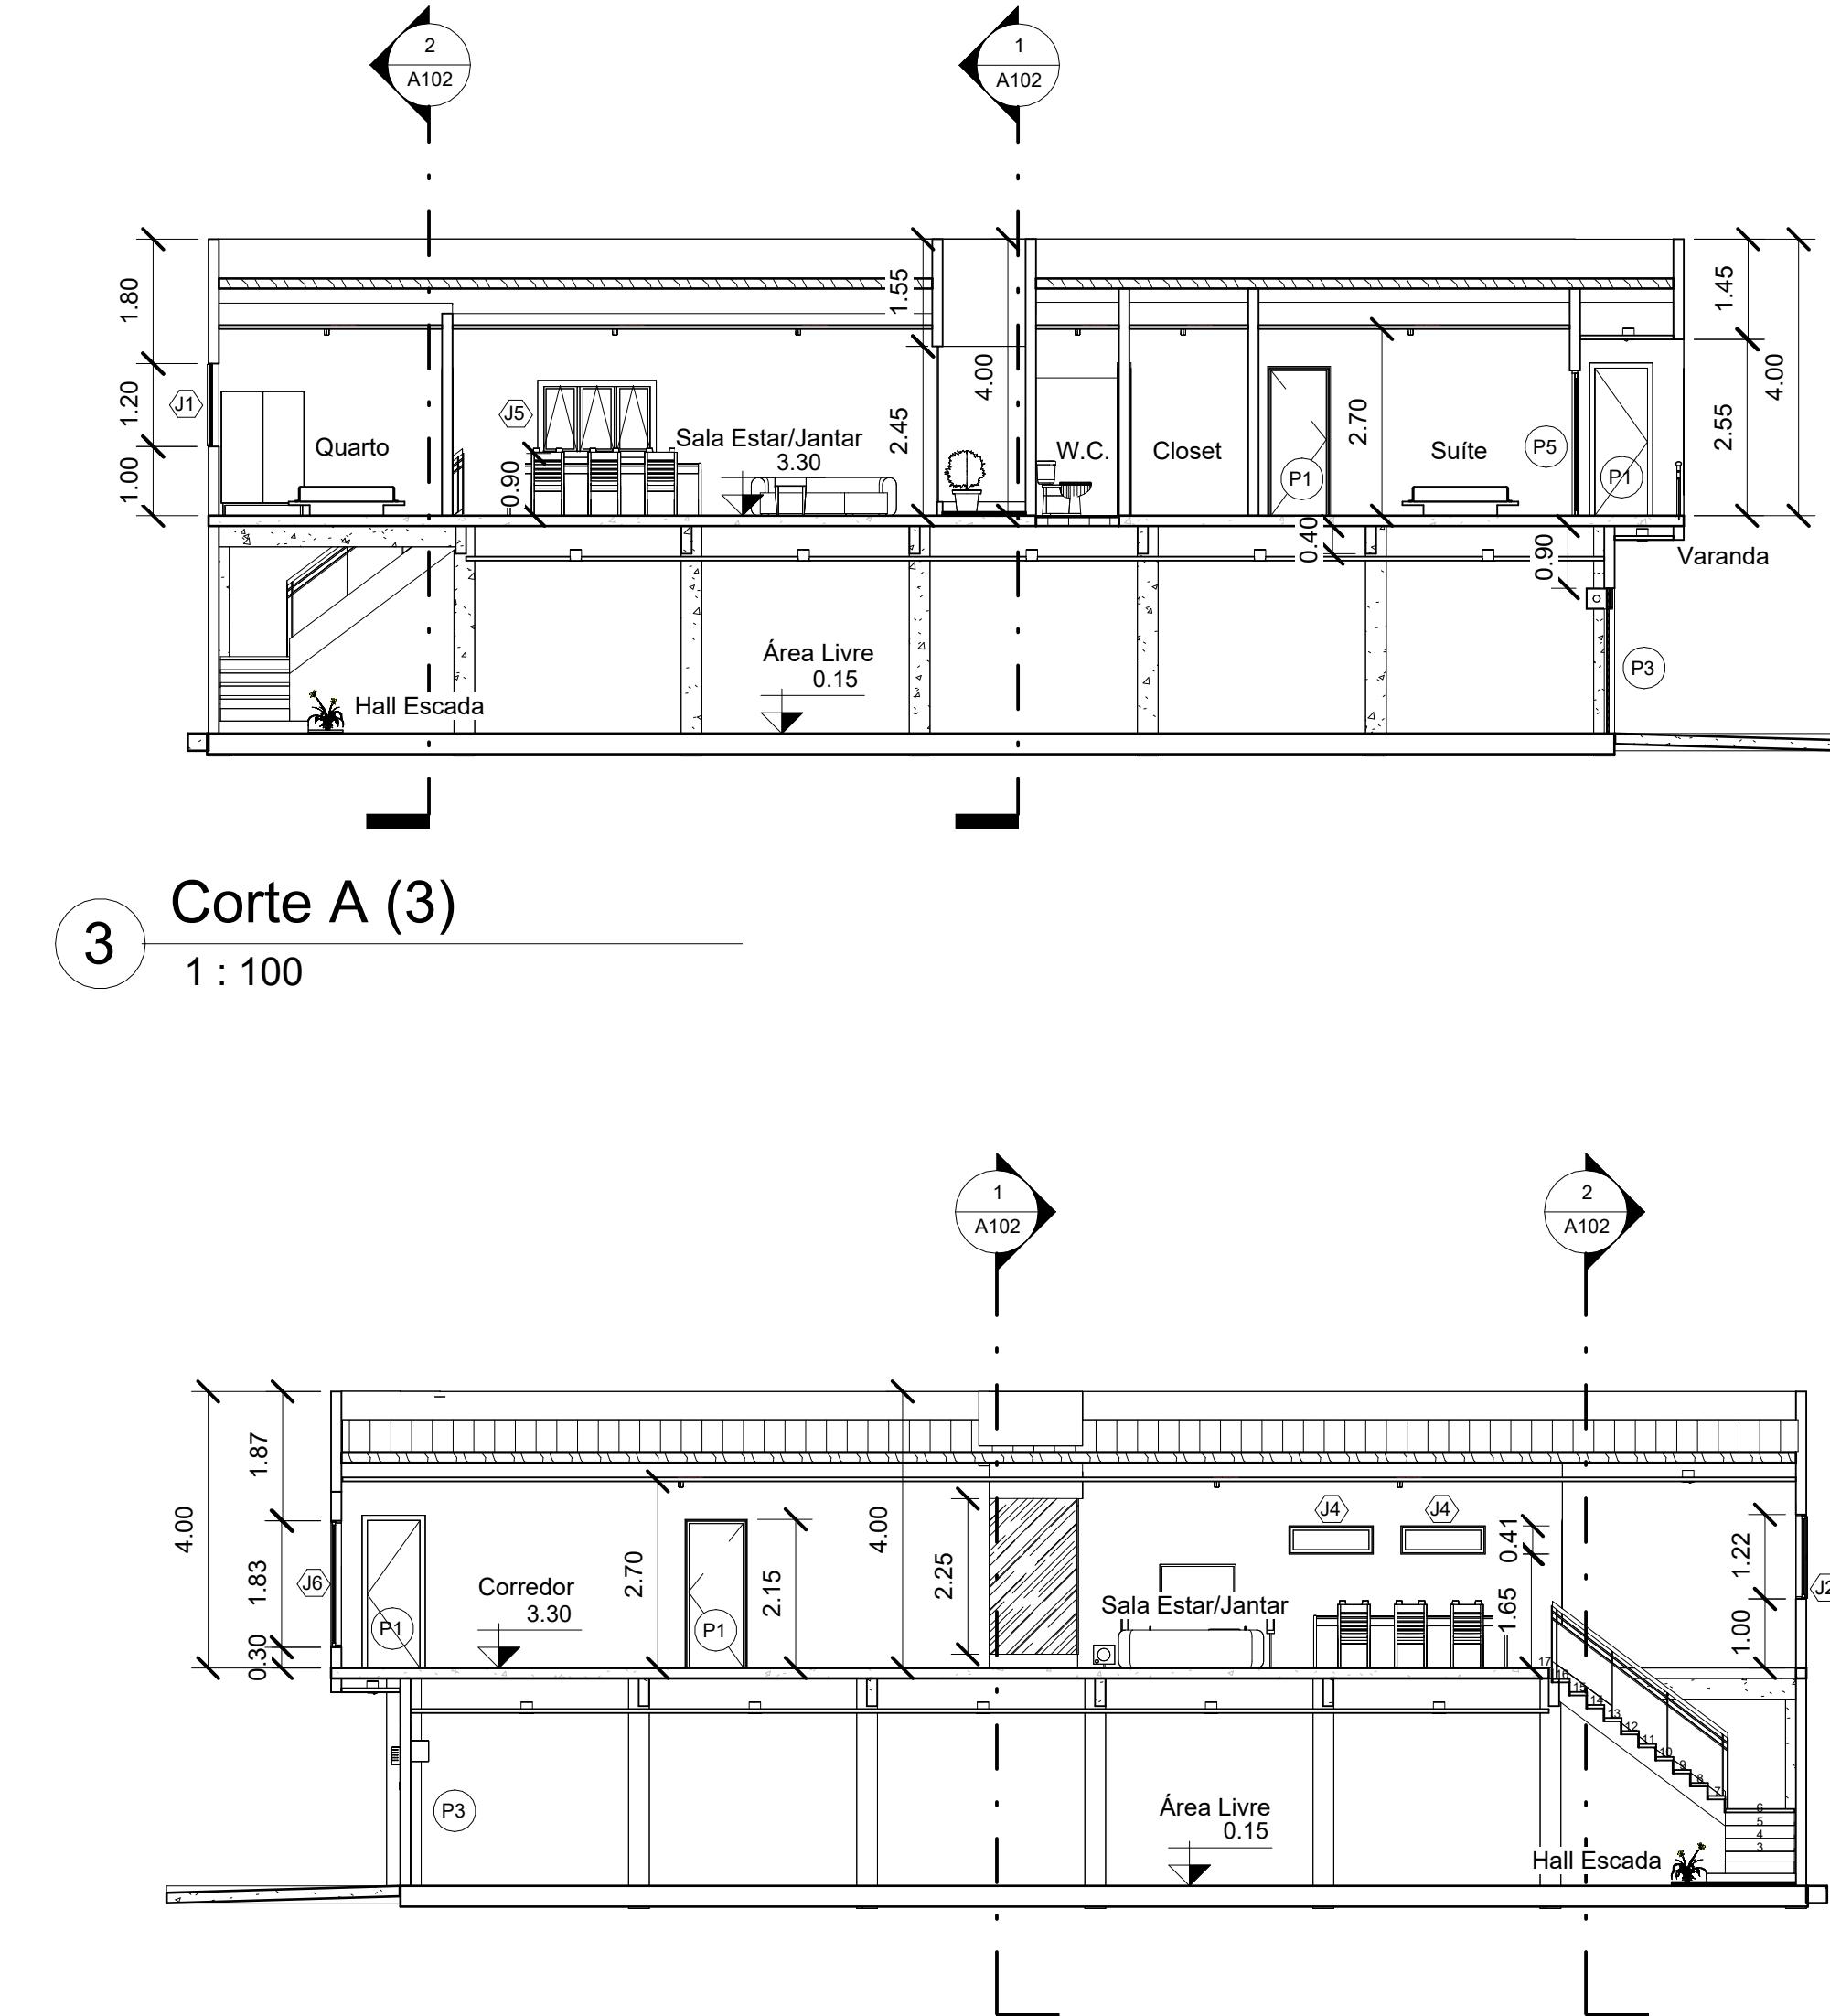

Corte B (4)
1 : 100

Quantidade de portas				
Contagem	Tipo	Largura	Altura	Marca
2	0.80 x 2.10 m	0.80	2.10	P1
1	3.00 x 2.10	3.00	2.10	P5
2	0762 x 2134mm	0.76	2.13	<varia>
1	Porta Enrolar 210x300	3.00	2.10	P3

Quantidade de janelas					
Contagem	Tipo	Largura	Altura	Descrição	Tipo de janela
1	0,60 x 0,60 m 2	0.60	0.60	Janela Basculante Maxim-Air	J3
2	1,2 x 0,4	1.22	0.41	Janela Basculante Maxim-Air	J4
1	1,20 x 1,20 m	1.20	1.20	Janela de Correr Vidro	J1
1	1.60 x 1.00	1.60	1.00	Janela Vidro 3 Folhas com Moldura	J5
1	0915 x 1220mm	0.92	1.22	Janela Fixa Vidro com Caixilho	J2
1	0915 x 1830mm	0.92	1.83	Janela Fixa Vidro com Caixilho	J6

Expansão Vertical (1 Pav)

FOLHA 01








Cliente: Antônio Erlendio Andrade de Mota

Data: 17/10/24

Desenhista: Niaggy S.Novo

Endereço: Rua Getúlio Vargas n177, Santo AntônioSanta Inês/MA

A101

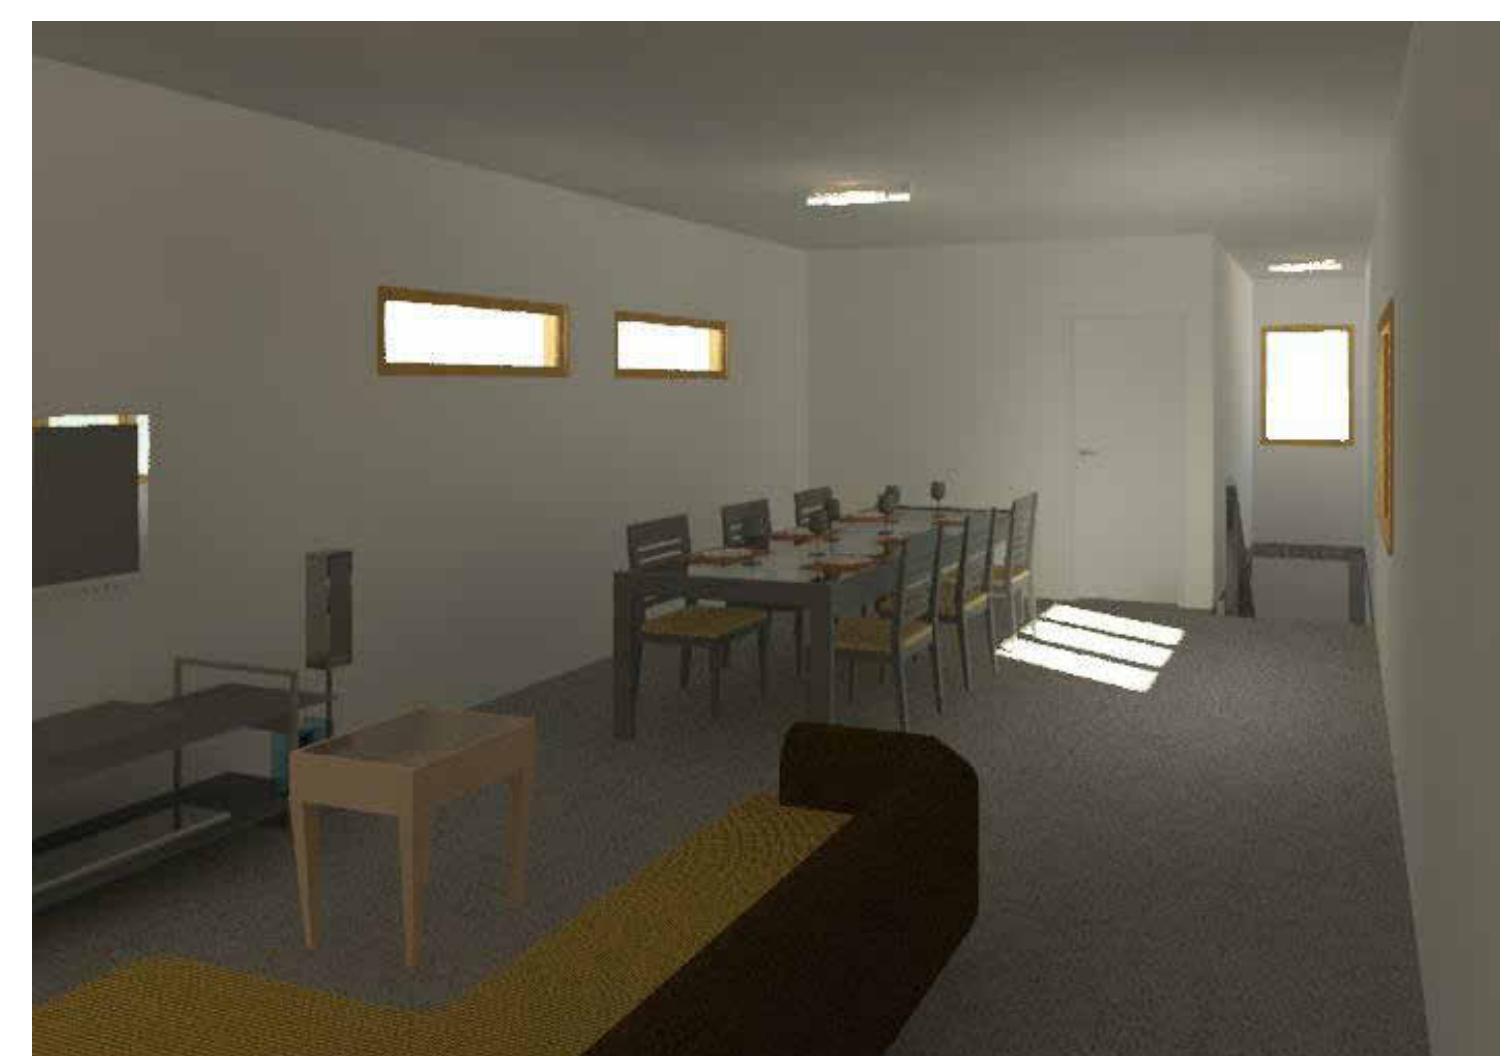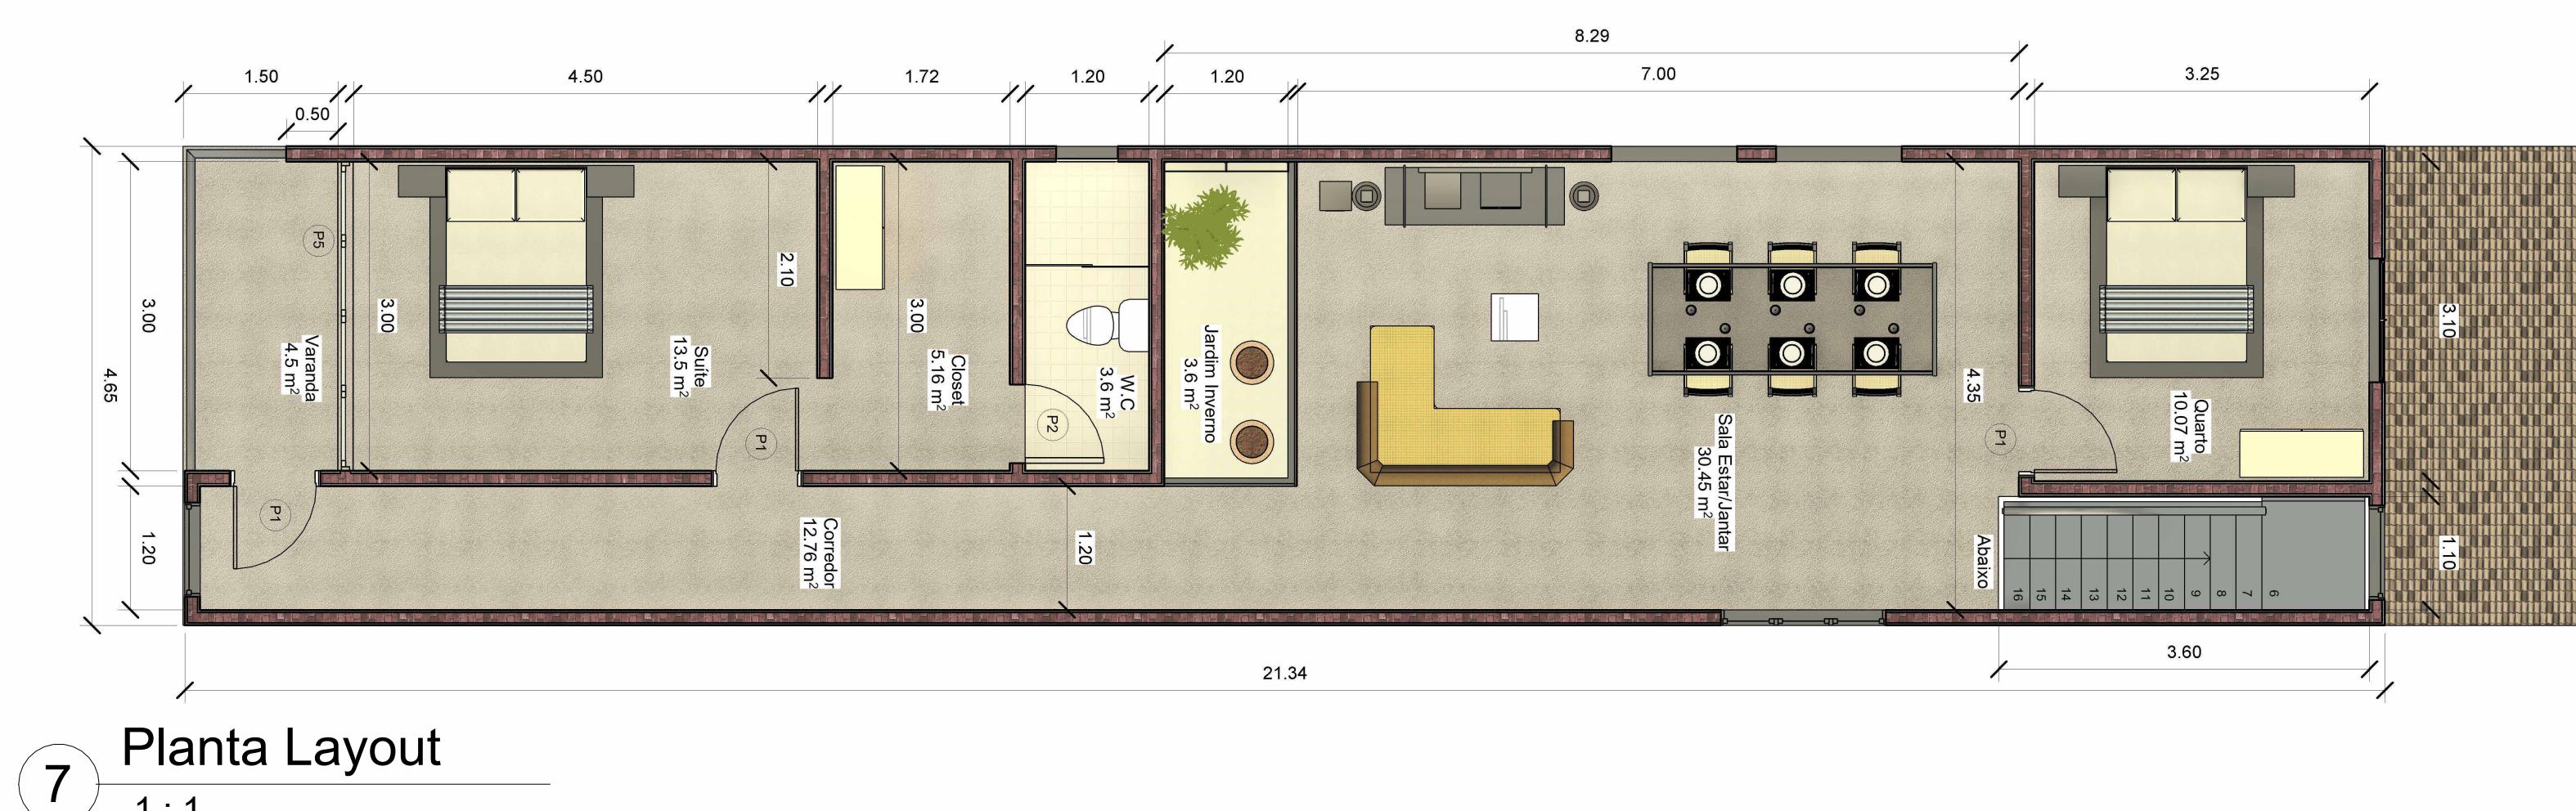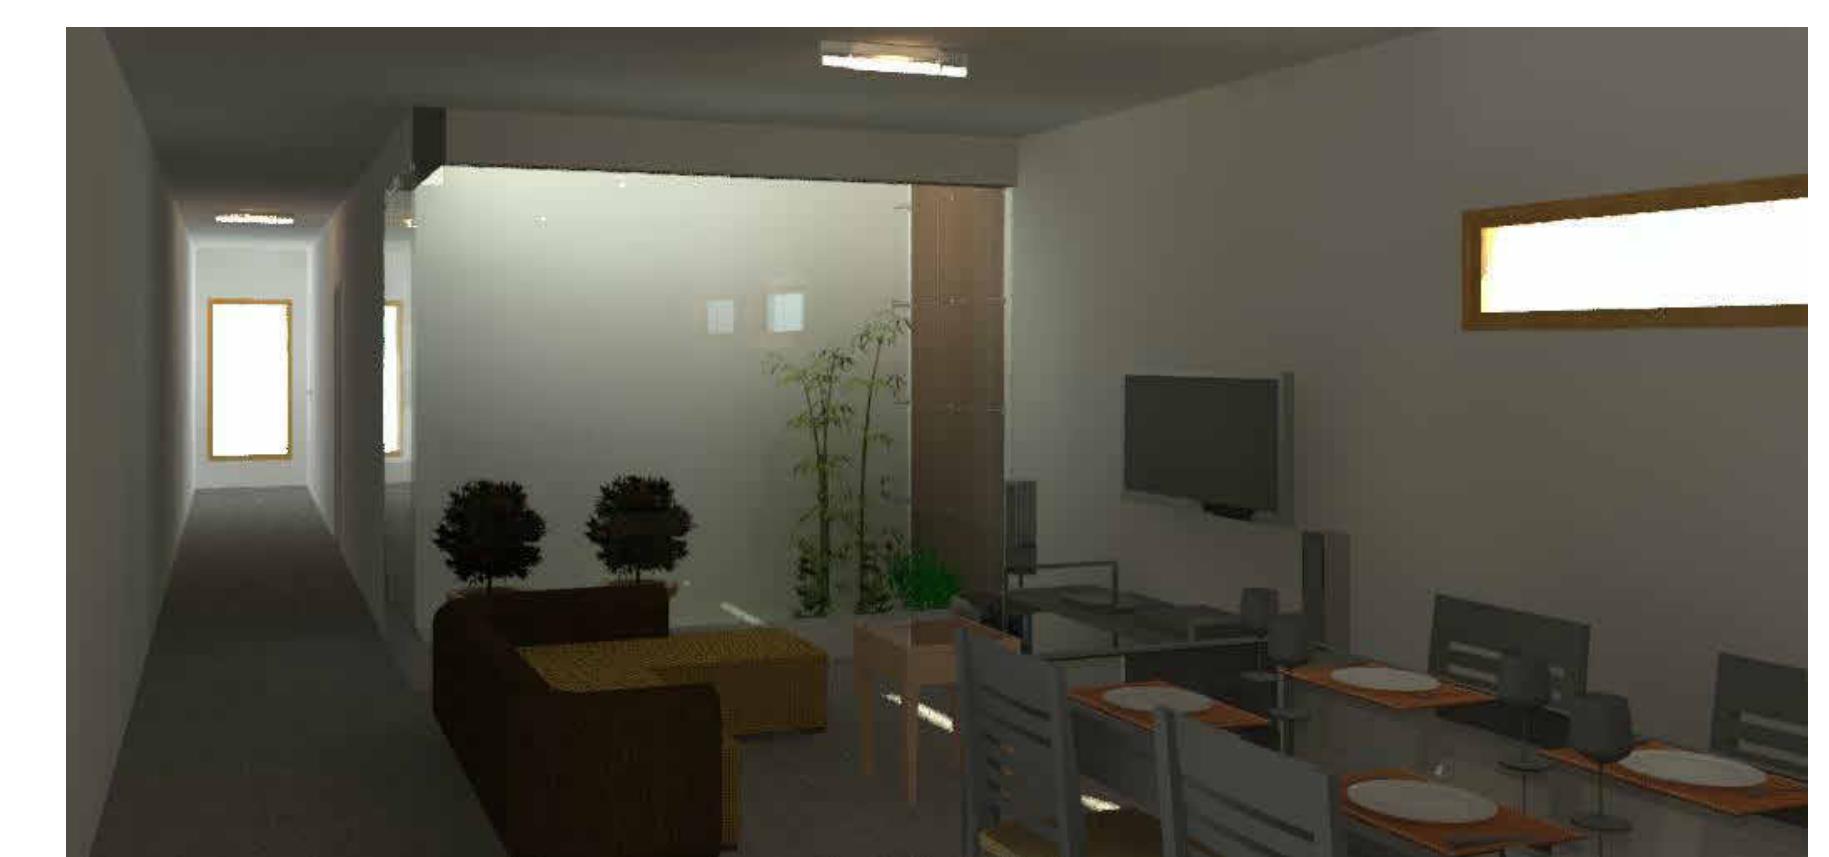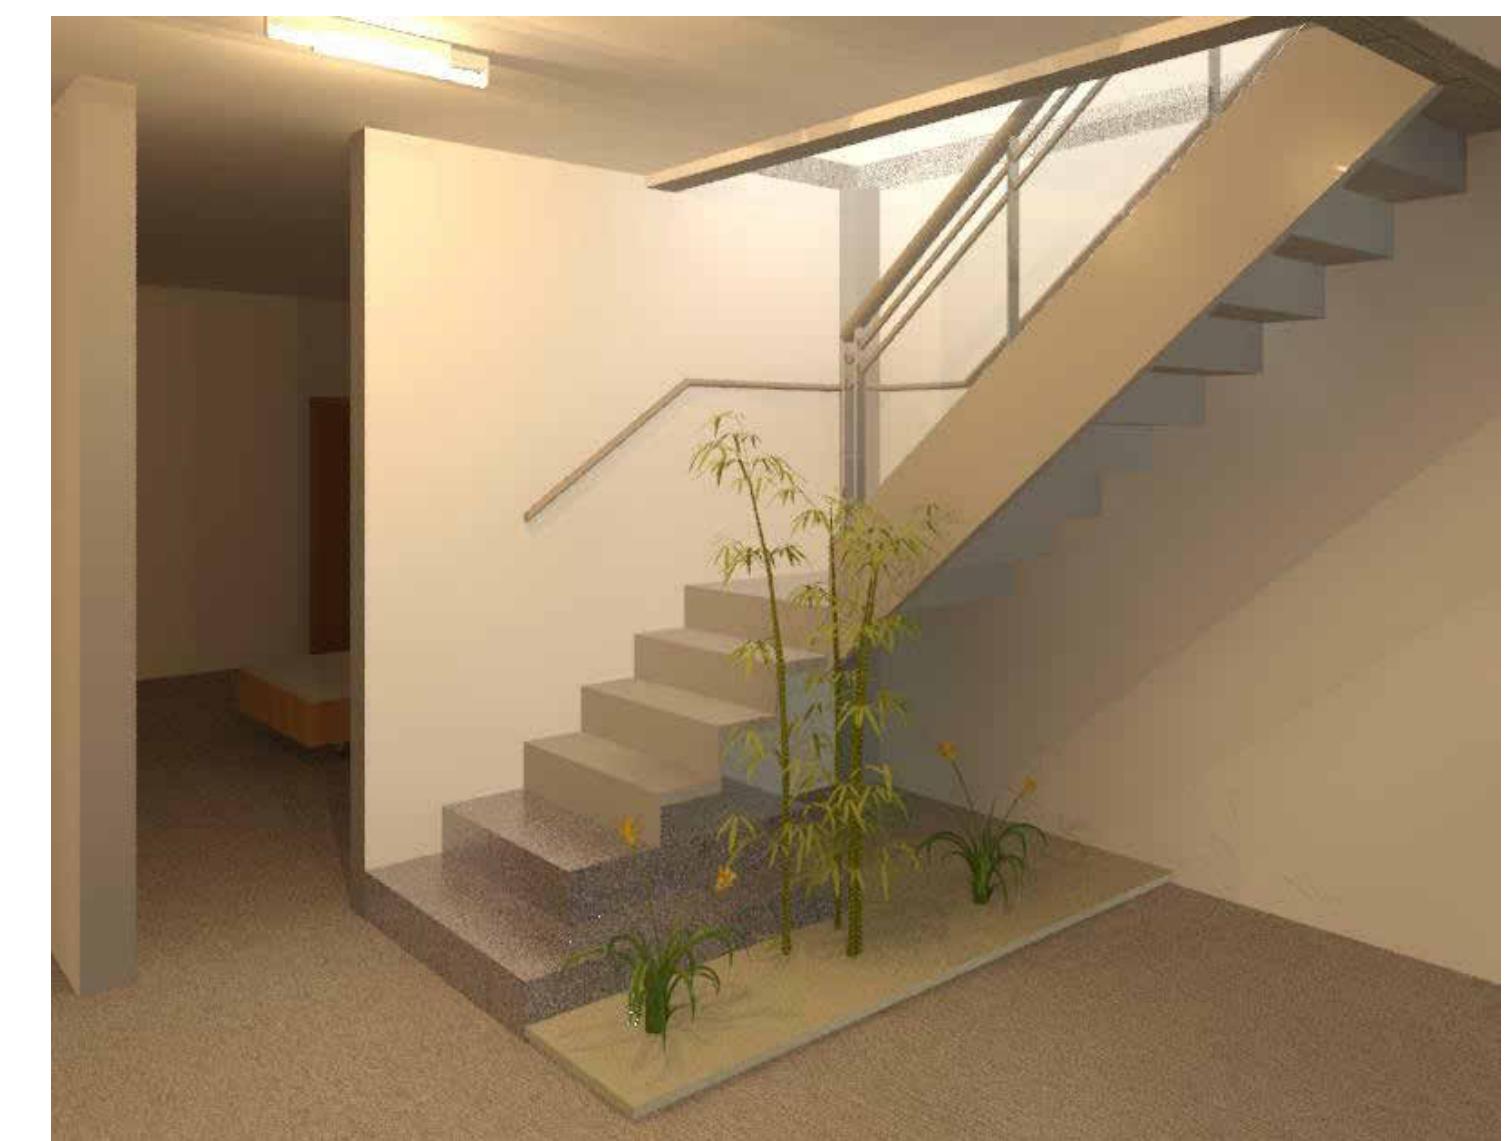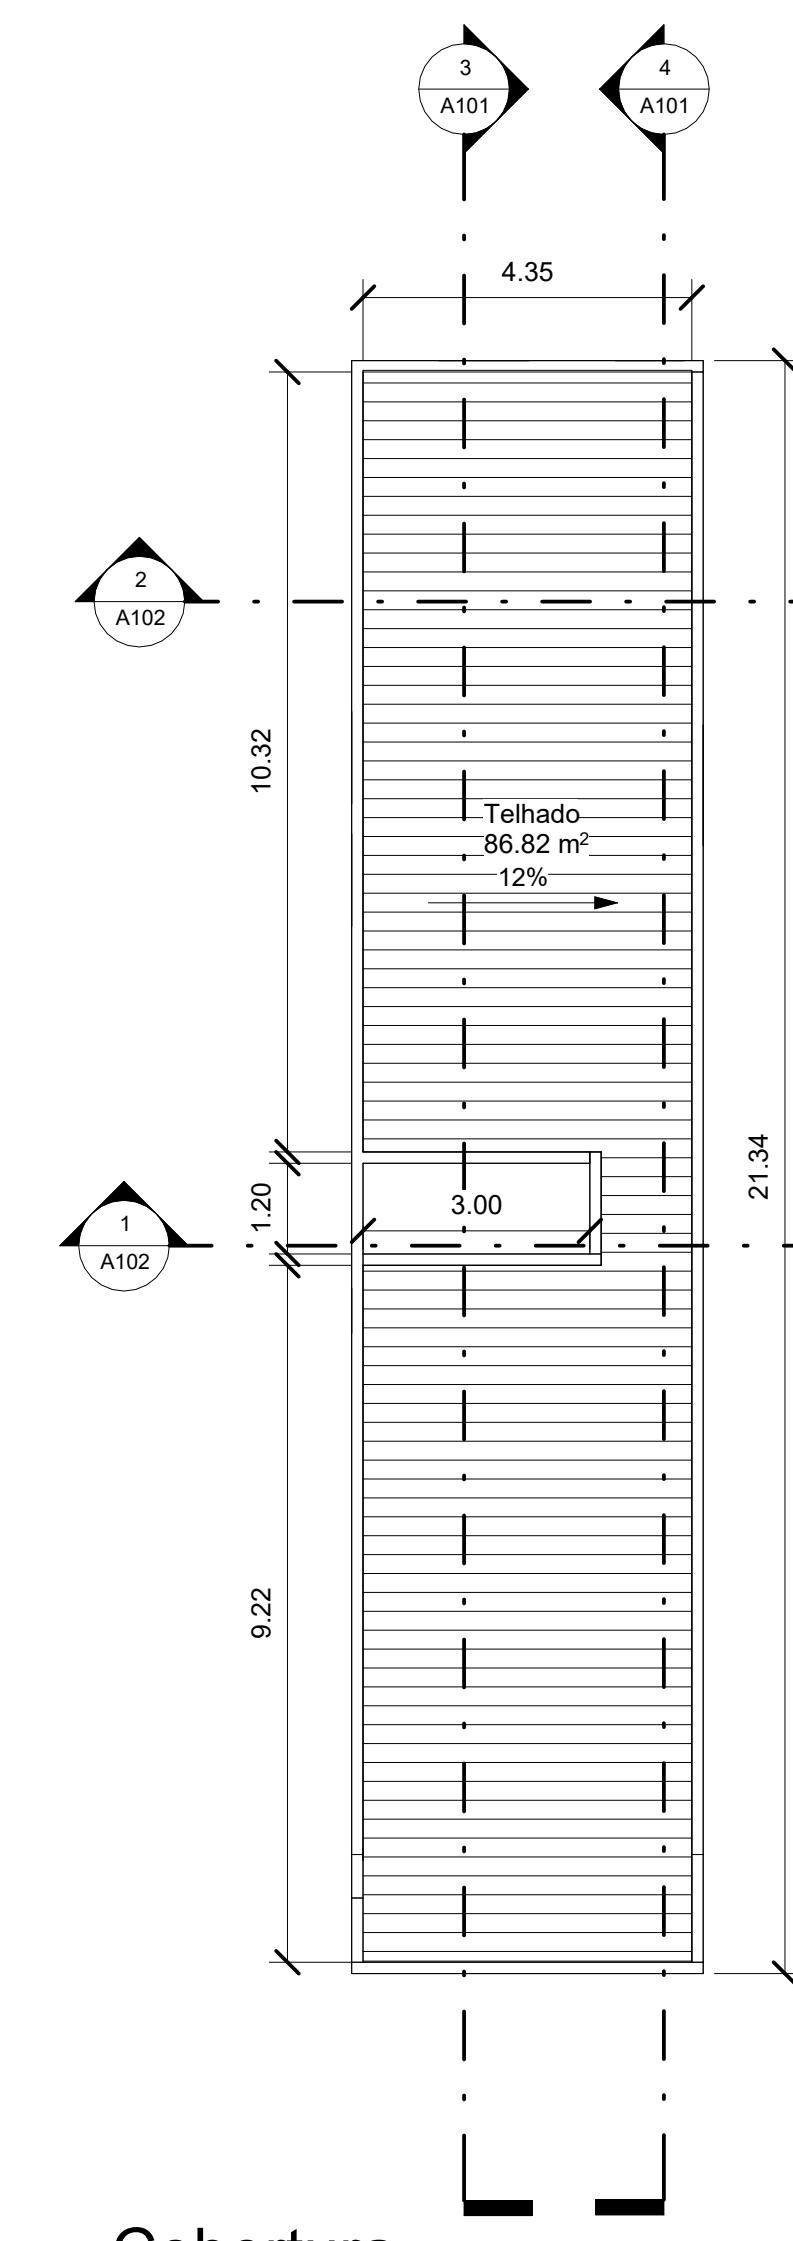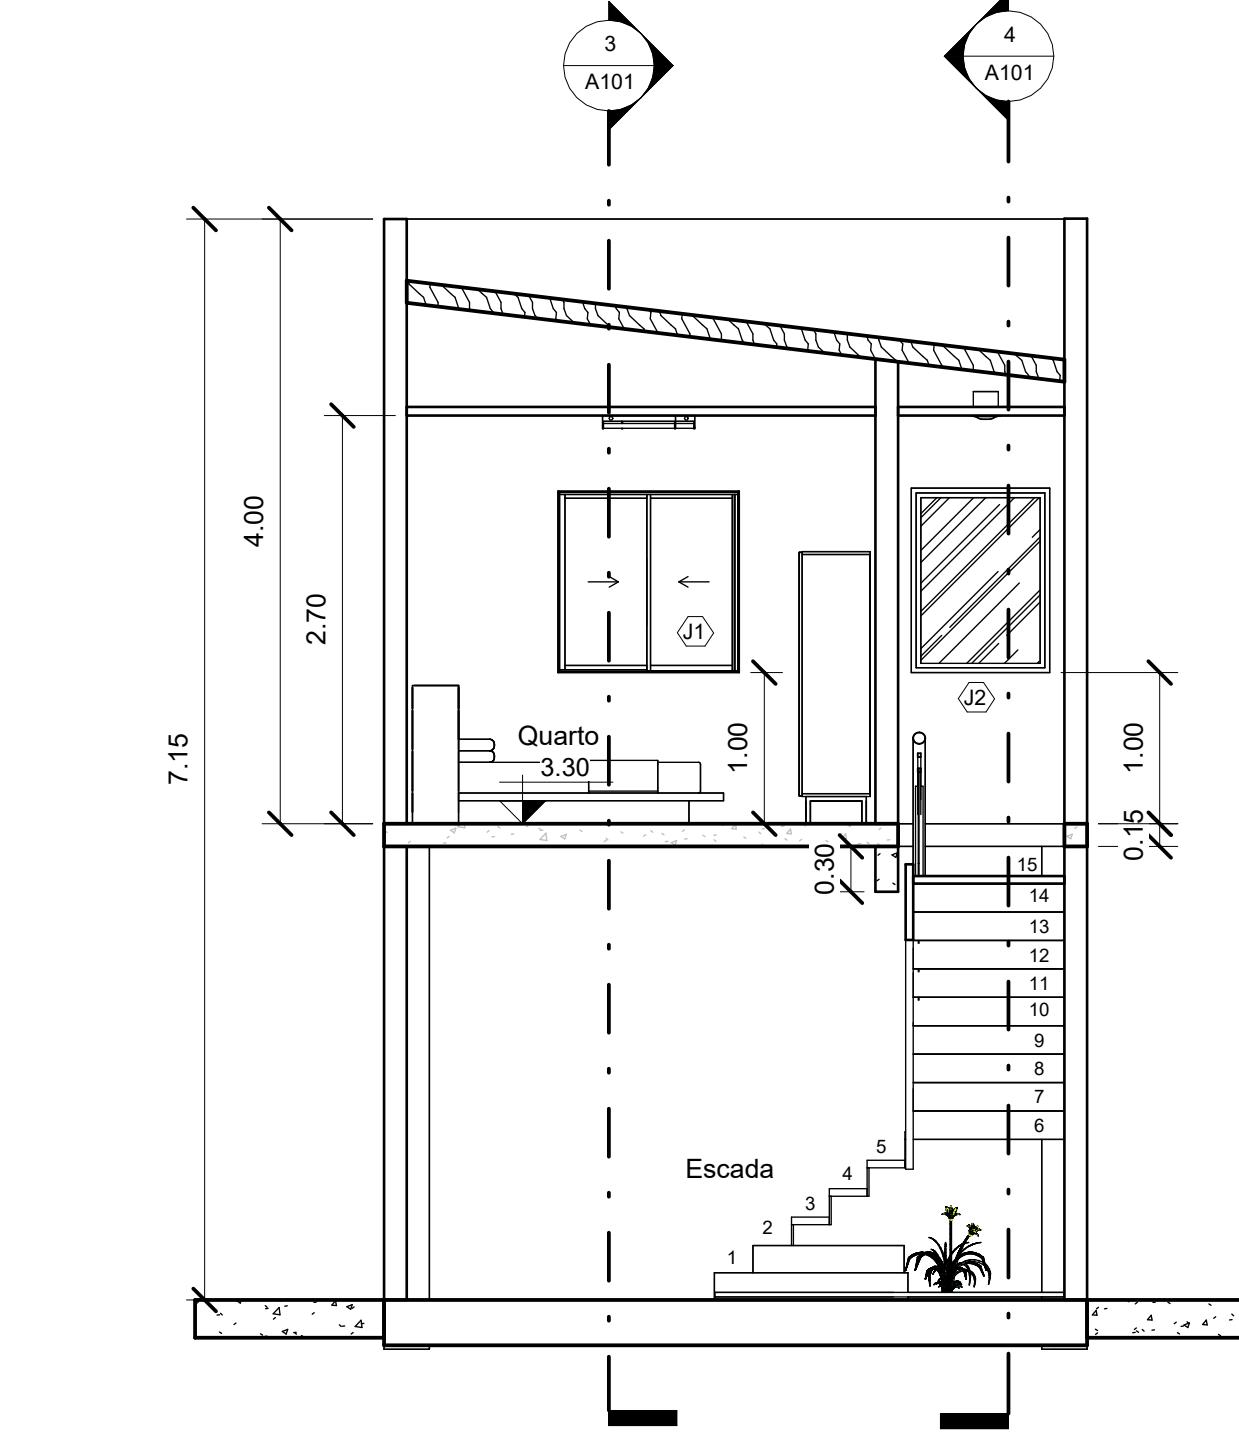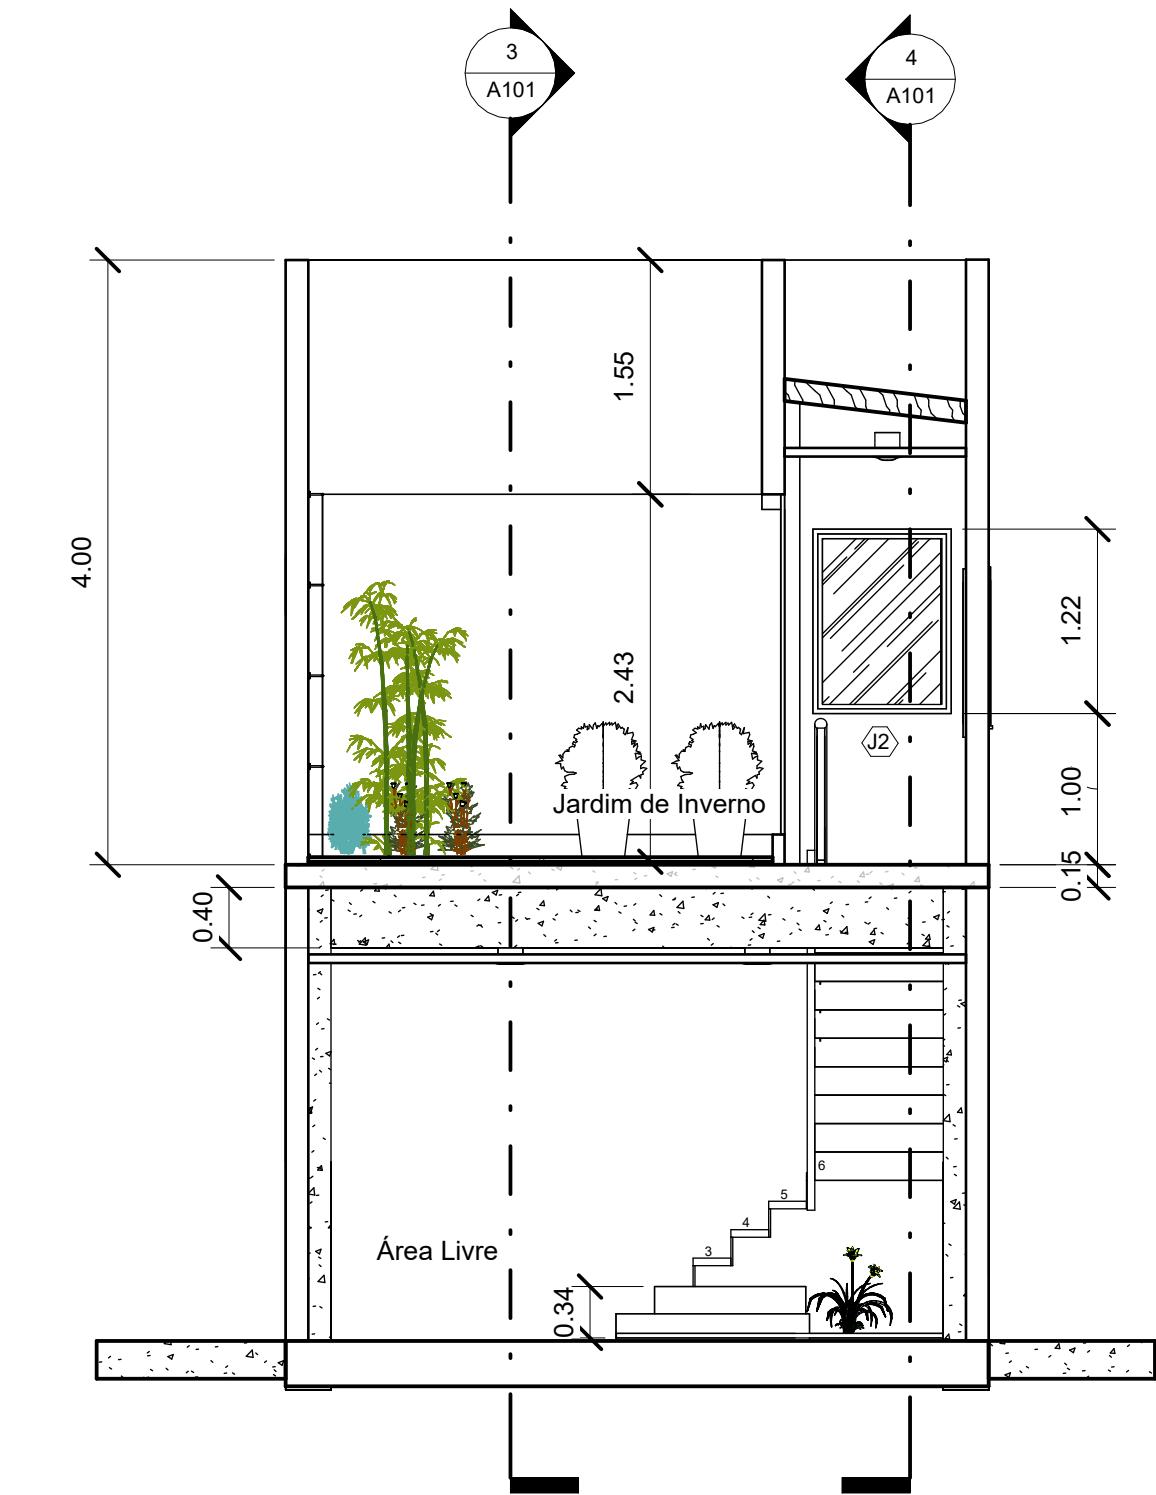

Expansão Vertical (1 Pav)

FOLHA 02

Cliente: Antonia Erlandia Andrade de Matos

Data: 17/10/24

Desenhista: Niaggy S. Novoa

Endereço: Rua Getúlio Vargas nº177, Santo Antônio Santa Inês/MA

A102


Escala Como indicado




1 Fachada Frontal
1 : 1




2 Fachada Lateral Leste
1 : 1

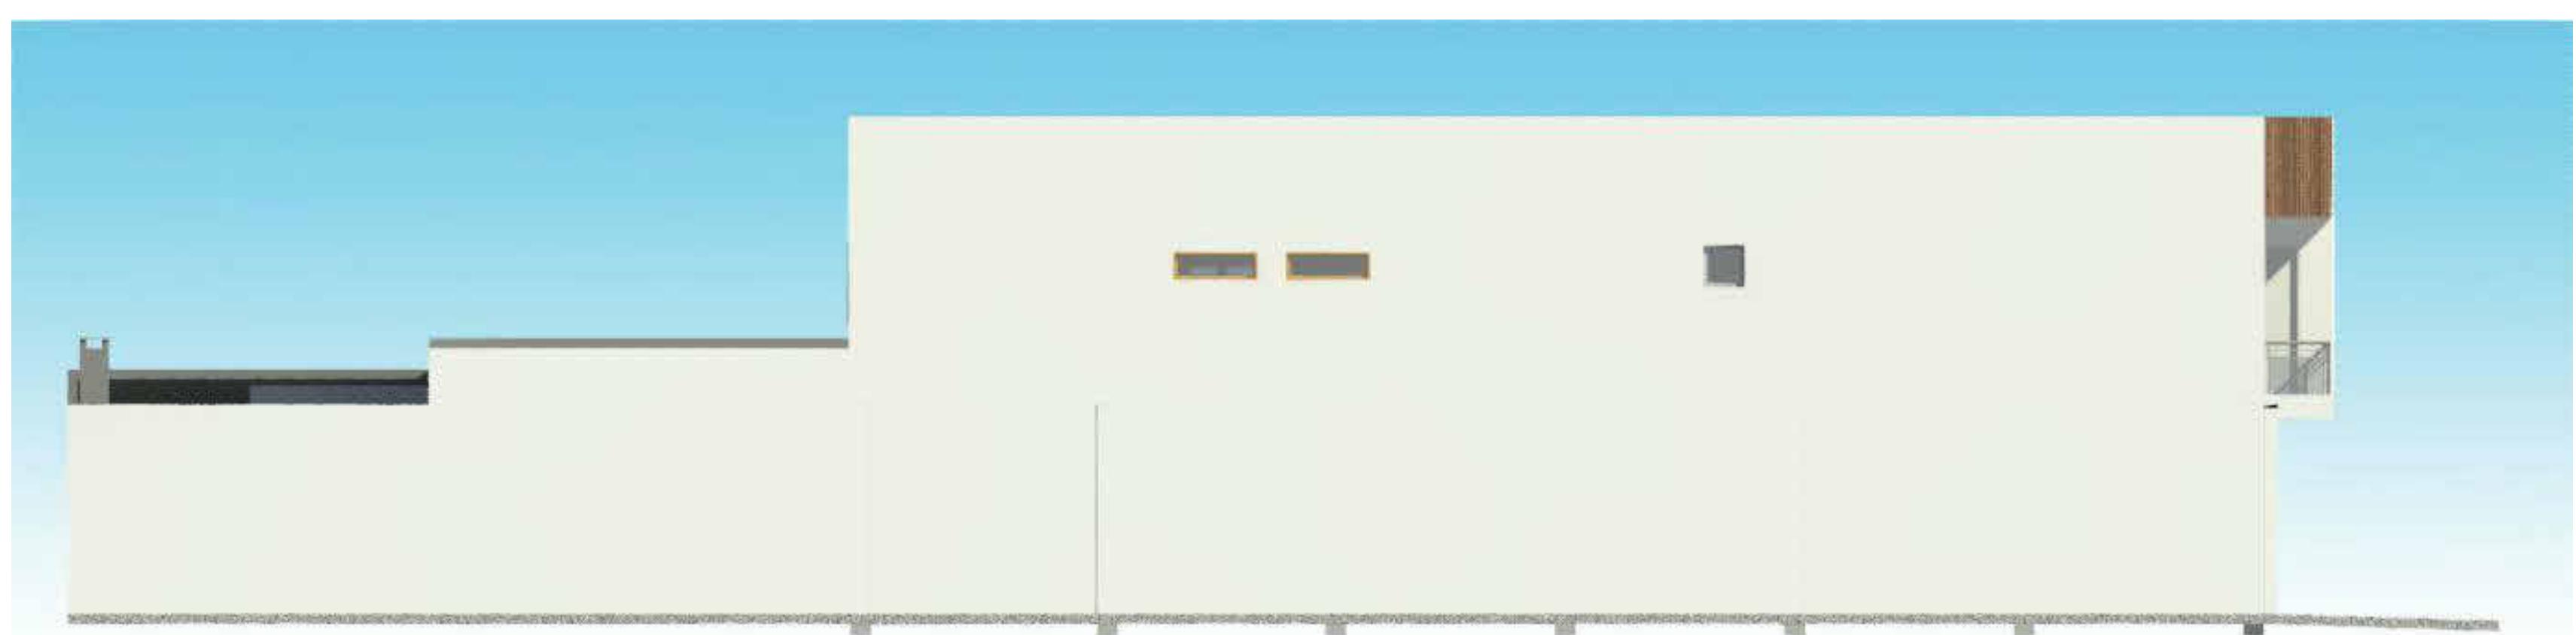

4 Fachada Lateral Oeste
1 : 1

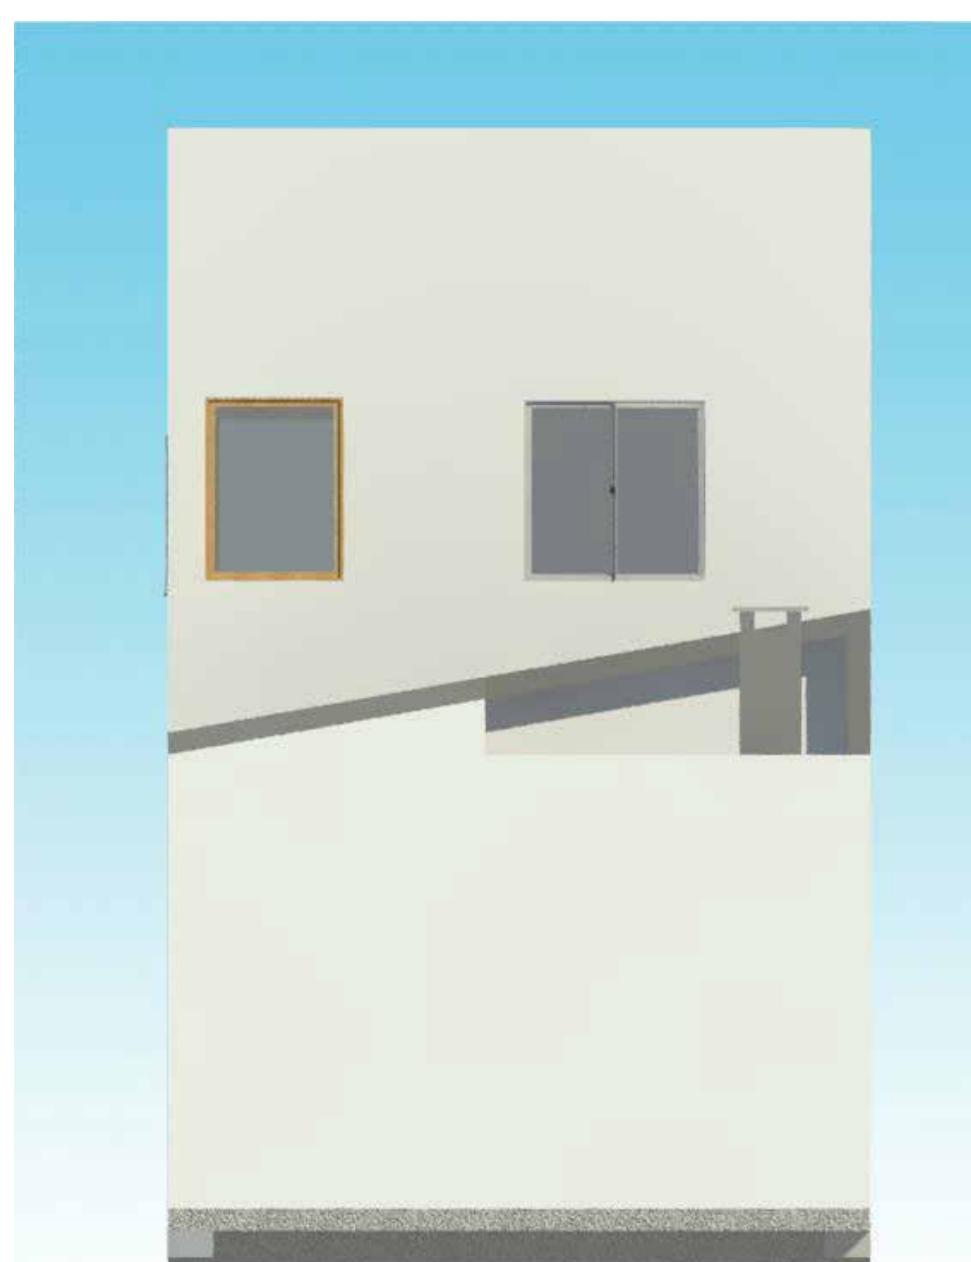

3 Fachada Fundos
1 : 1

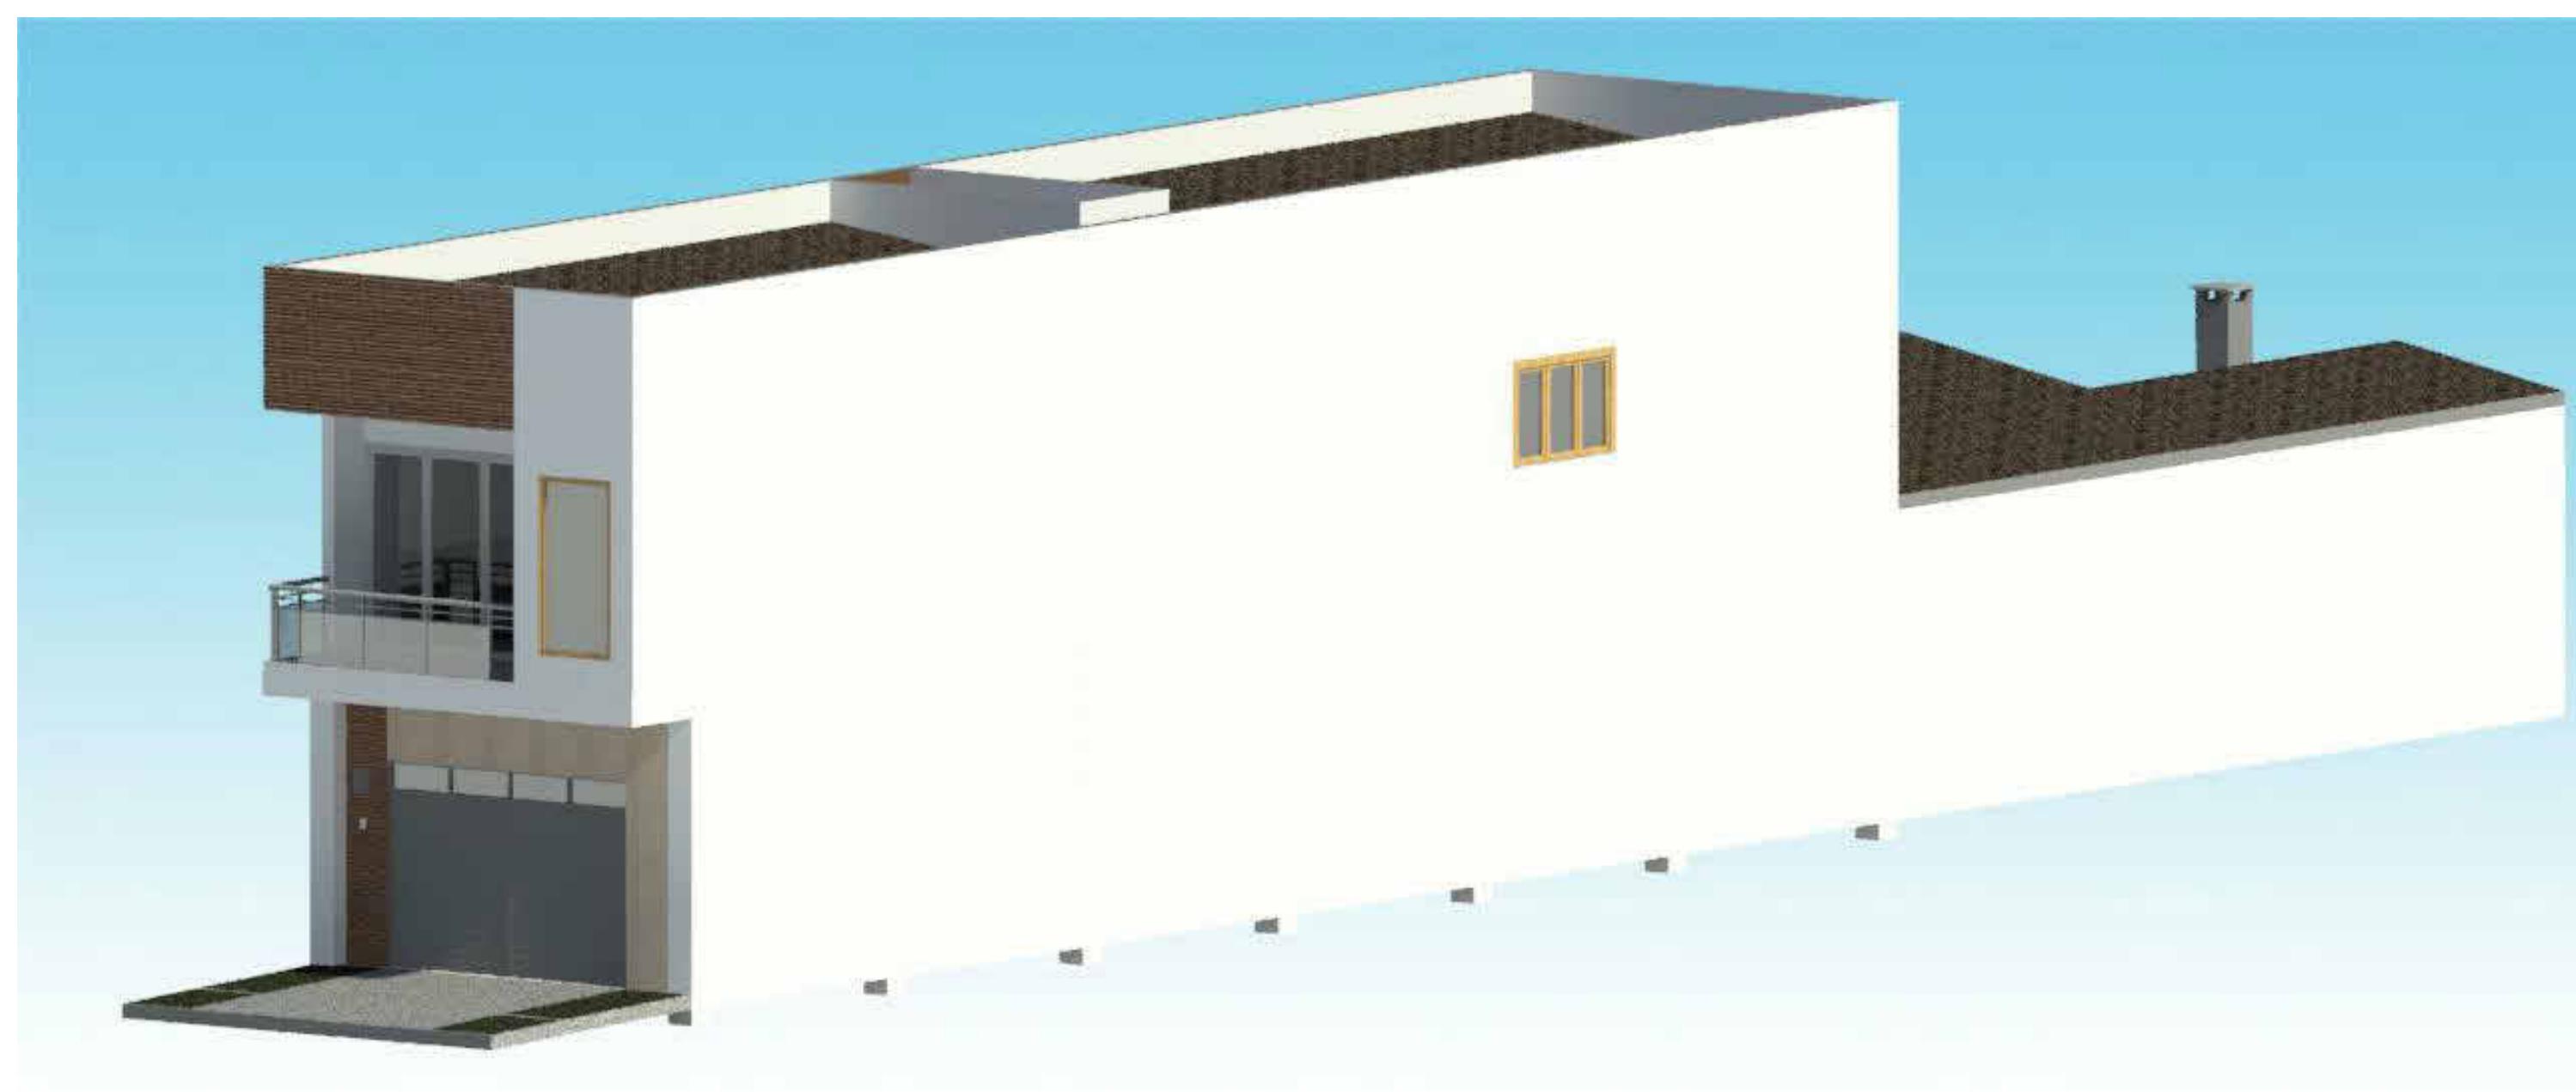

5 Vista Superior Frontal
1 : 1

Expansão Vertical (1 Pav)

FOLHA 03

Cliente: Antonia Erlandia Andrade de Matos

Data: 17/10/24

Desenhista: Niaggy S.Novoa

Endereço: Rua Getúlio Vargas n°177, Santo Antônio Santa Inês/MA

A104

Escala 1 : 1